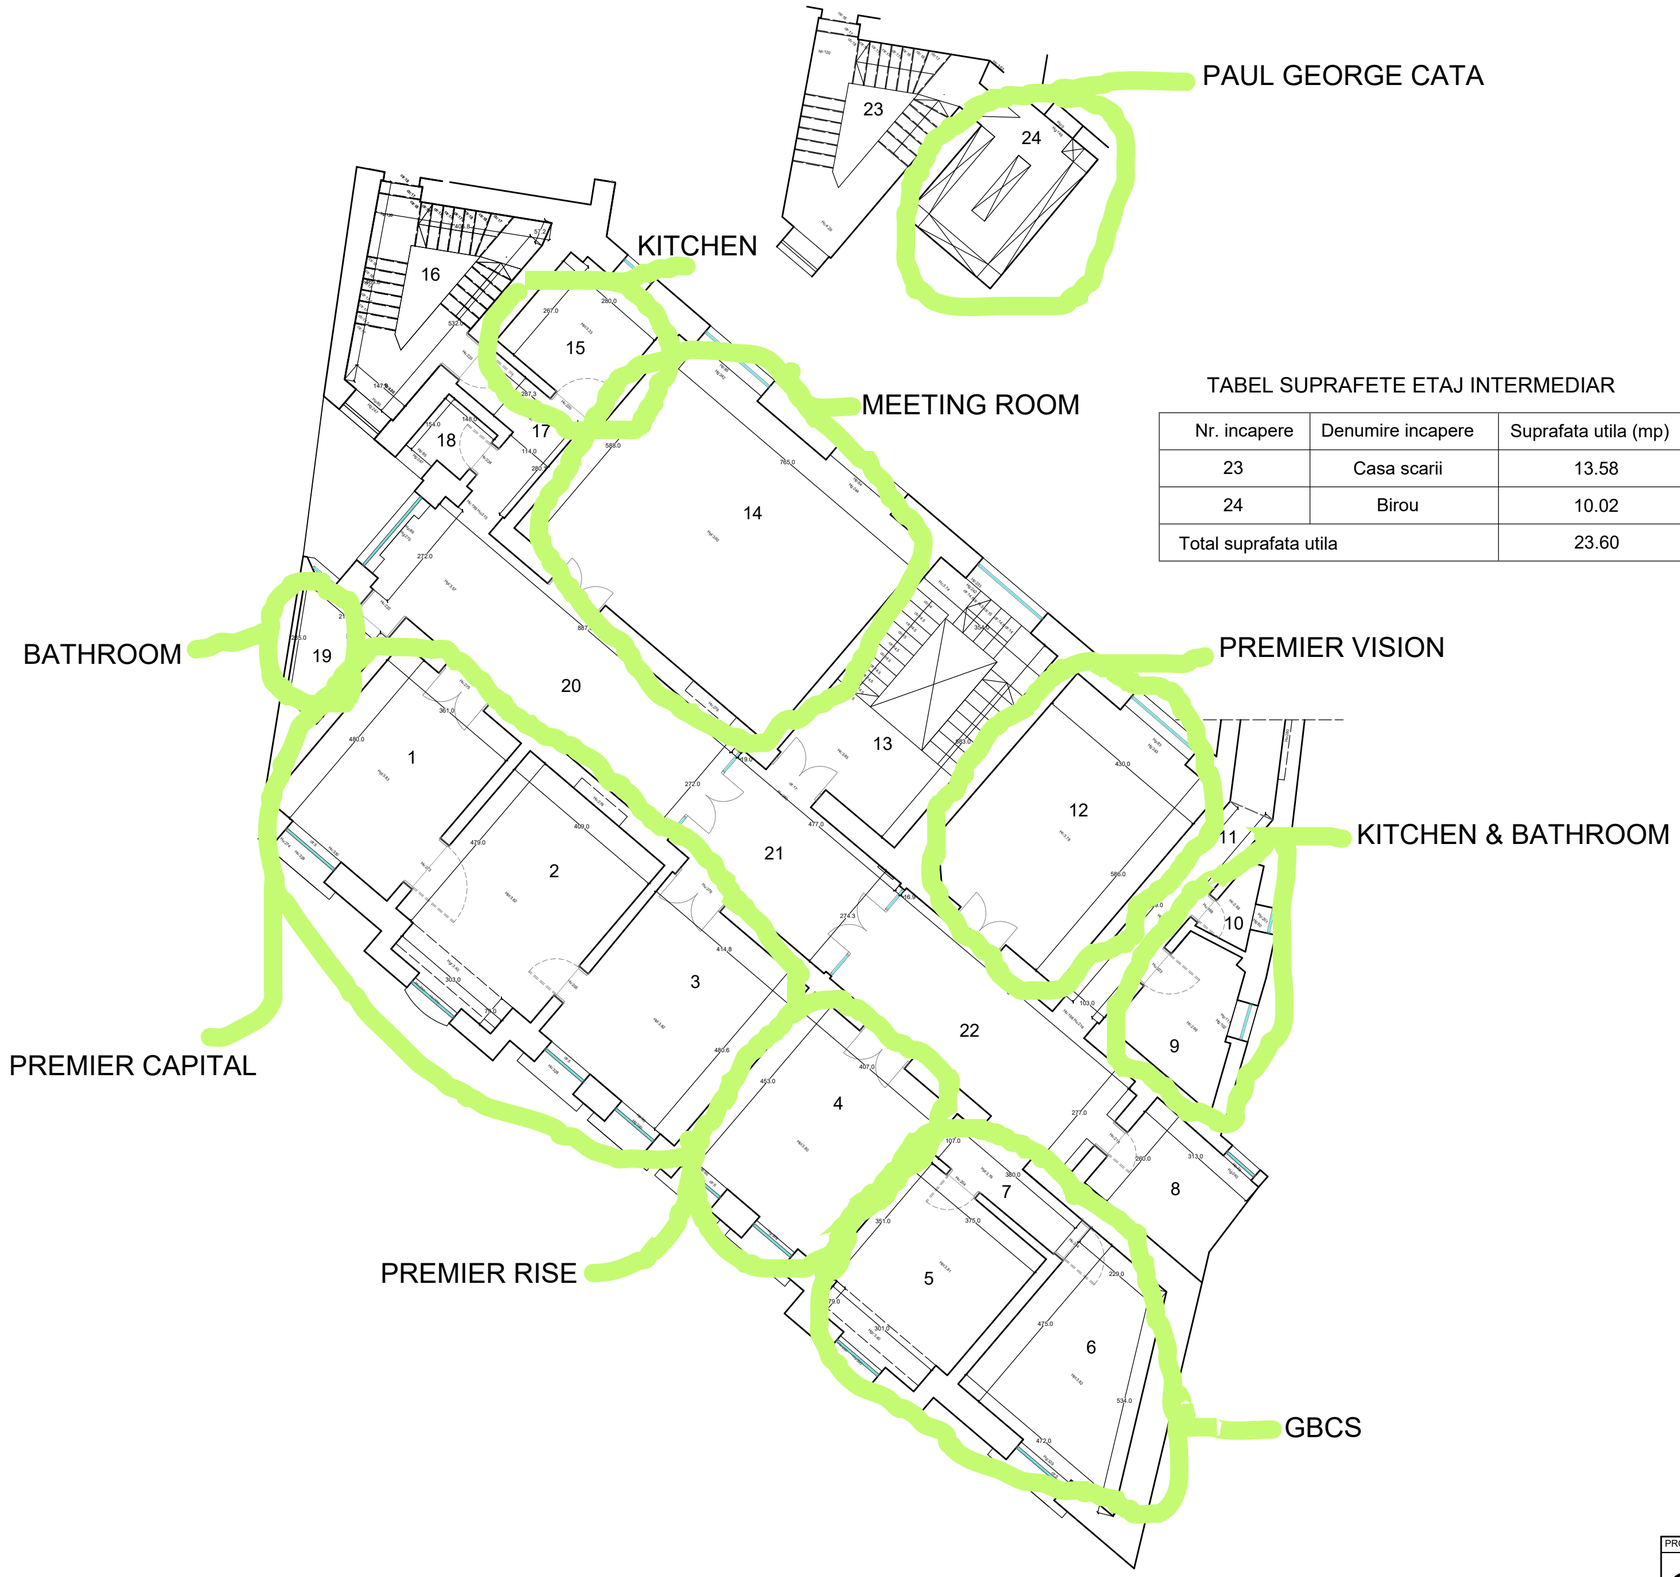

TABEL SUPRAFETE ETAJ INTERMEDIAR

Nr. incapere	Denumire incapere	Suprafata utila (mp)
23	Casa scarii	13.58
24	Birou	10.02
Total suprafata utila		23.60

TABEL SUPRAFETE - ETAJ 1

Nr. incapere	Denumire incapere	Suprafata utila (mp)
1	Birou	17.28
2	Birou	21.98
3	Birou	19.81
4	Birou	19.52
5	Birou	15.73
6	Birou	16.74
7	Sas	4.00
8	Birou	8.32
9	Baie	7.70
10	W.C.	1.59
11	Hol	6.68
12	Birou	25.23
13	Casa scarii	20.69
14	Birou	44.98
15	Bucatarie	7.84
16	Casa scarii	13.92
17	Hol	5.18
18	Grup sanitar	2.00
19	Grup sanitar cu dus	4.39
20	Hol	24.91
21	Hol	13.03
22	Hol	19.66
Total suprafata utila		299.53

C4
Etaj 1
S construita:736.97 mp

PROIECTANT ARHITECTURA				BENEFICIAR:	
S.C. GAIA PROJECT S.R.L. Str. Pictor Th. Aman nr.16, sector 1, Bucuresti, Romania J21/280/2016 CUI 36241450				RGI OFFICES	PR. NR. A102/2022
				PROIECT:	
				ADRESA: Bucuresti, sector 5, Blvd. Mihail Kogalniceanu, nr.12	
SPECIFICATIE	NUME	SEMNATURA	SCARA 1:100	PLANȘA: C4- PLAN ETAJ 1	FAZA: D.T.A.C.
COORDONARE:	arh. Ghabrah Mouanes				
PROIECTAT:	arh. Ghabrah Muhamed-Dib		DATA 2022		PL. NR. A07
DESENAT:	arh. Teodorescu Cezar				